



PUENTE PEATONAL



ALCALDÍA DE
MOSQUERA



CONSTRUCCION PUENTE PEATONAL



ALCALDÍA DE
MOSQUERA



AREA DE INFLUENCIA



ALCALDÍA DE
MOSQUERA




CONDICIONALES PARA LA UBICACION




ALCALDÍA DE
MOSQUERA



SECCION ARQUITECTURA

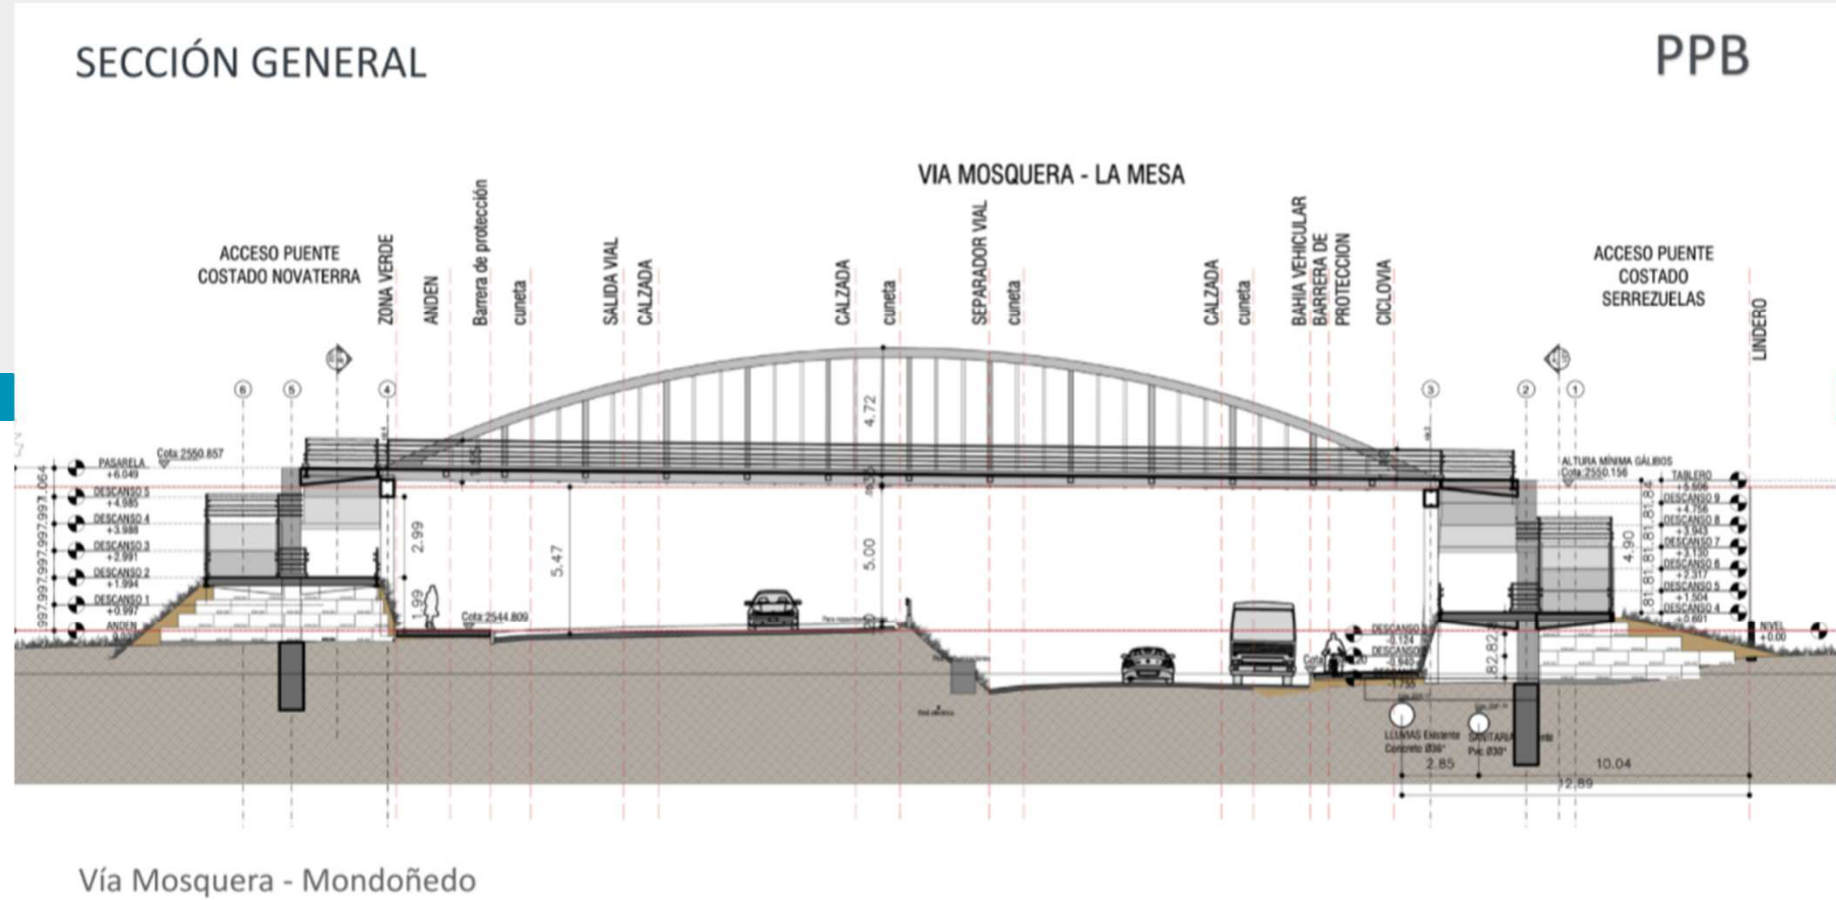

ESTRUCTURA PUENTE PEATONAL

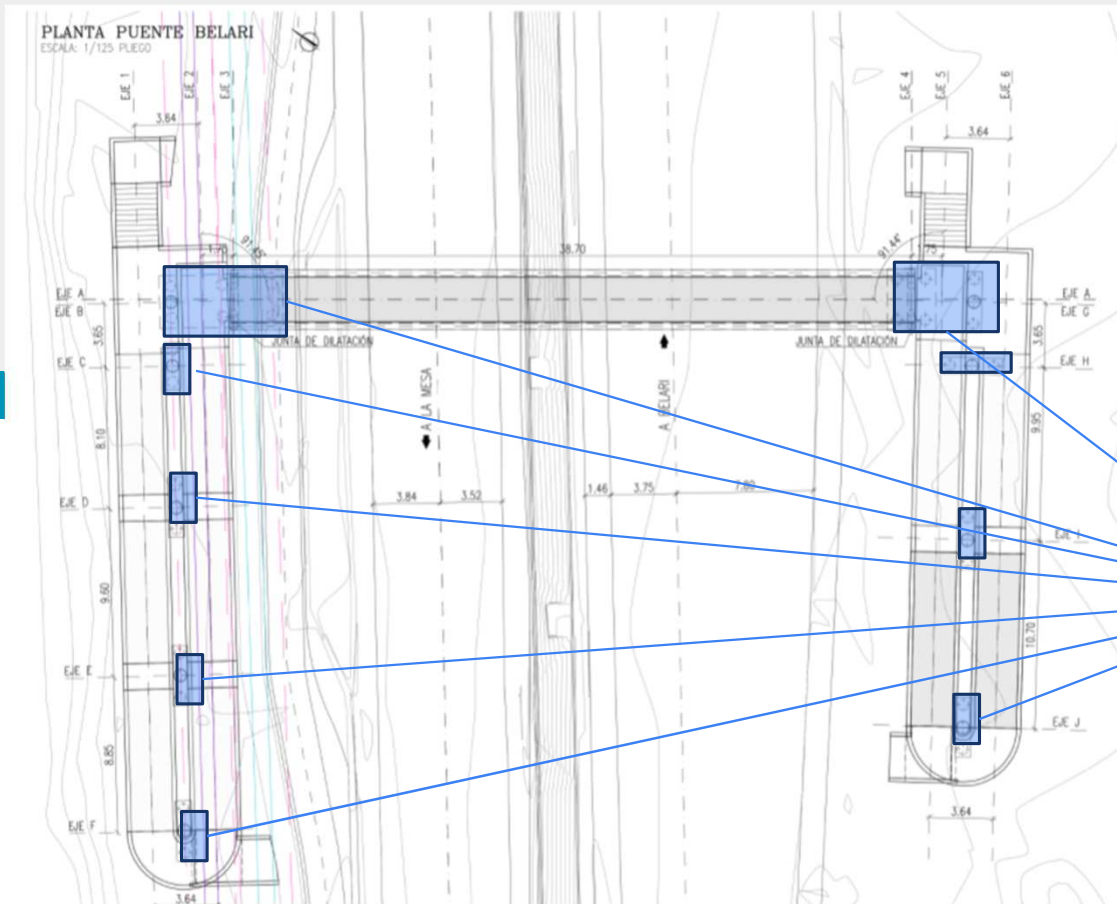

Pilotes a 25 y 30 metros de profundidad, diámetro de 60 cm. Con tipología de dados para el soporte de las columnas.




ALCALDÍA DE
MOSQUERA



ESTRUCTURA PUENTE PEATONAL

FASE I

ESCALA: 1/100 PLIEGO
ESCALA: 1/250 A3

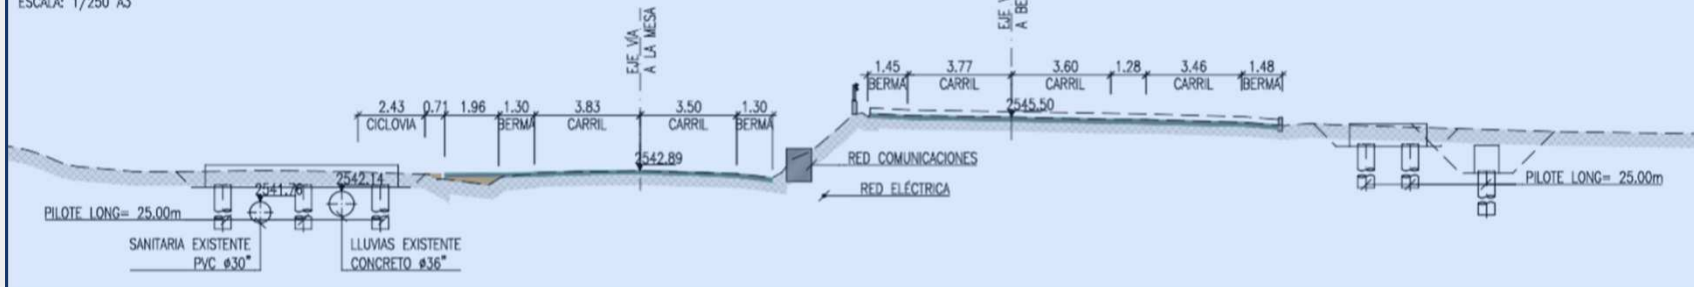


FASE I:

1. EXCAVACIÓN, ARMADO Y HORMIGONADO PILOTES TENIENDO EN CUENTA LAS REDES EXISTENTES.
 2. EXCAVACIÓN, ARMADO Y HORMIGONADO DADOS TENIENDO EN CUENTA LAS REDES EXISTENTES.
- CORTES DE TERRENO INDICATIVOS, PODRÍAN LLEGARSE A REQUERIR OBRAS DE PROTECCIÓN Y/O SOSTENIMIENTO EN FUNCIÓN DE LA ALTURA DEL CORTE, ÉSTA CONDICIÓN DEBERÁ SER DISEÑADA Y VALORADA POR EL INGENIERO GEOTECNISTA DEL PROYECTO.

FASE II

ESCALA: 1/100 PLIEGO
ESCALA: 1/250 A3

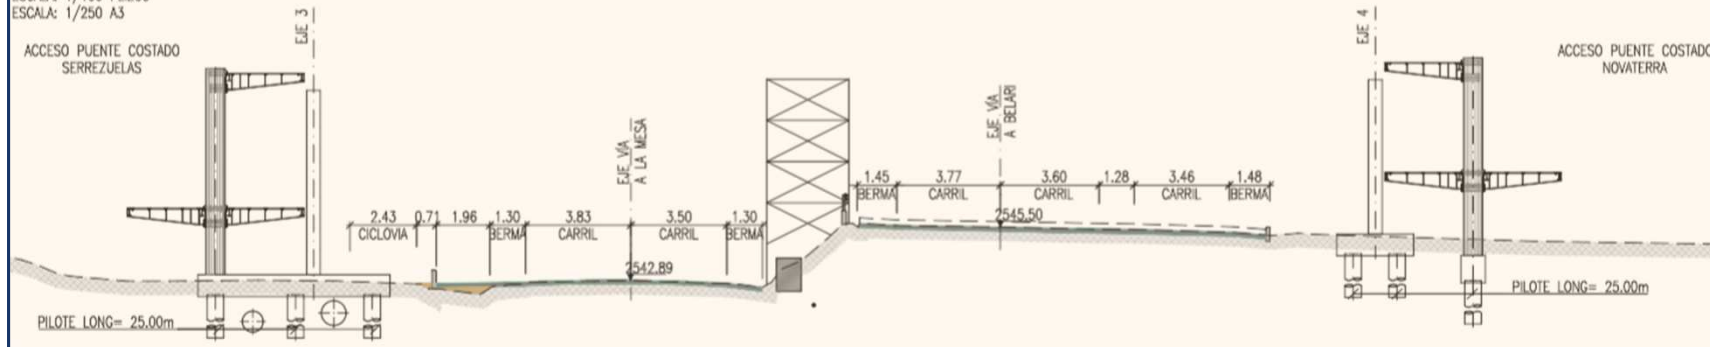

FASE II:

1. ARMADO Y HORMIGONADO PILAS.
2. ARMADO Y HORMIGONADO DE ZONAS DE ARRANQUE PARA RAMPAS.
3. INSTALACIÓN DE MÉNSULAS METÁLICAS DE APOYOS PARA RAMPAS.
4. INSTALACIÓN DE APOYO TEMPORAL PARA SOSTENER LA ESTRUCTURA DE LA PASARELA EN LA MITAD DEL VANO.




ALCALDÍA DE
MOSQUERA



MOSQUERA
CAMPO DE GIGANTES

ESTRUCTURA PUENTE PEATONAL

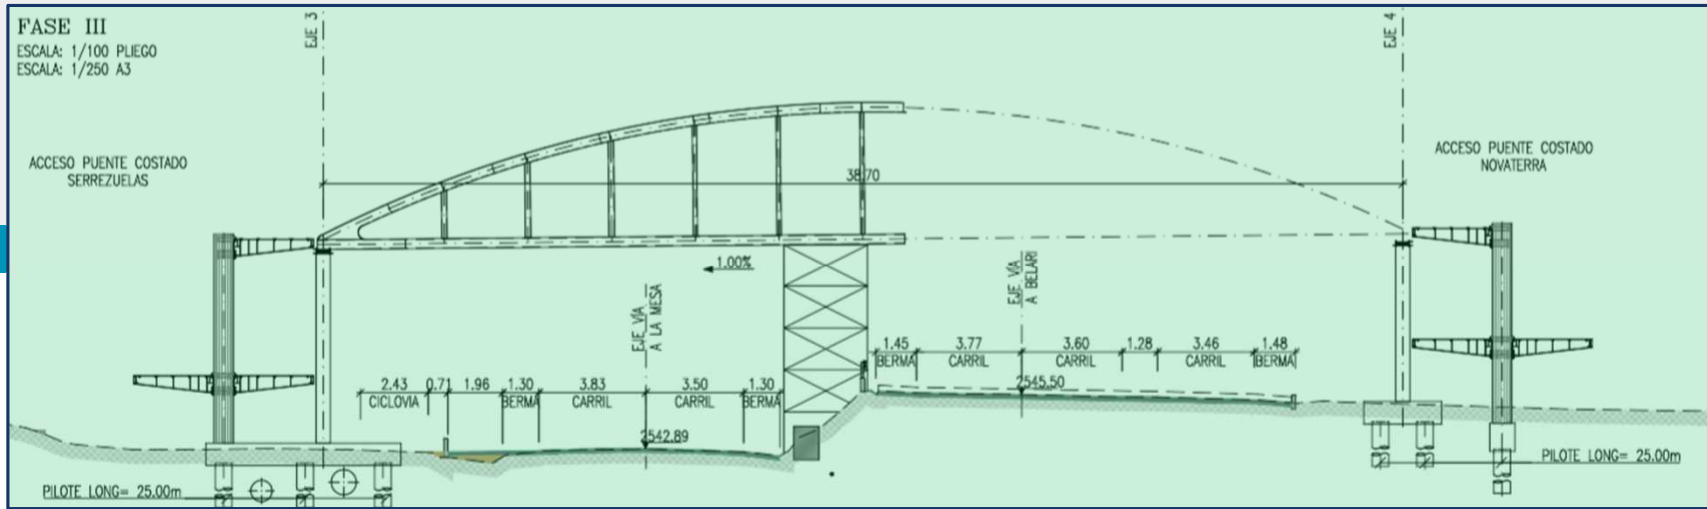

FASE III:


1. INSTALACIÓN DE APARATOS DE APOYO.
2. IZAJE DE PRIMERA PARTE DEL ARCO, PREVIAMENTE ARMADO.



ALCALDÍA DE
MOSQUERA




ESTRUCTURA PUENTE PEATONAL

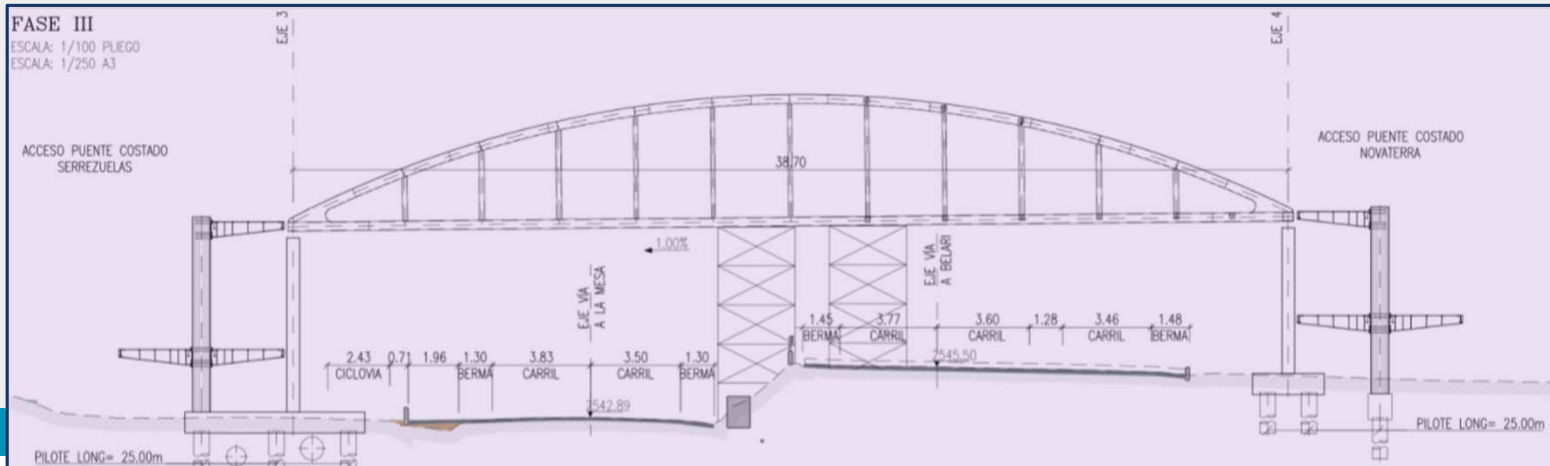

FASE III:

1. IZAJE DE SEGUNDA PARTE DEL ARCO PREVIAMENTE ARMADO.
2. ARMADO DE LA ESTRUCTURA DE LAS RAMPAS
3. ARMADO Y HORMIGONADO DE ESCALERAS

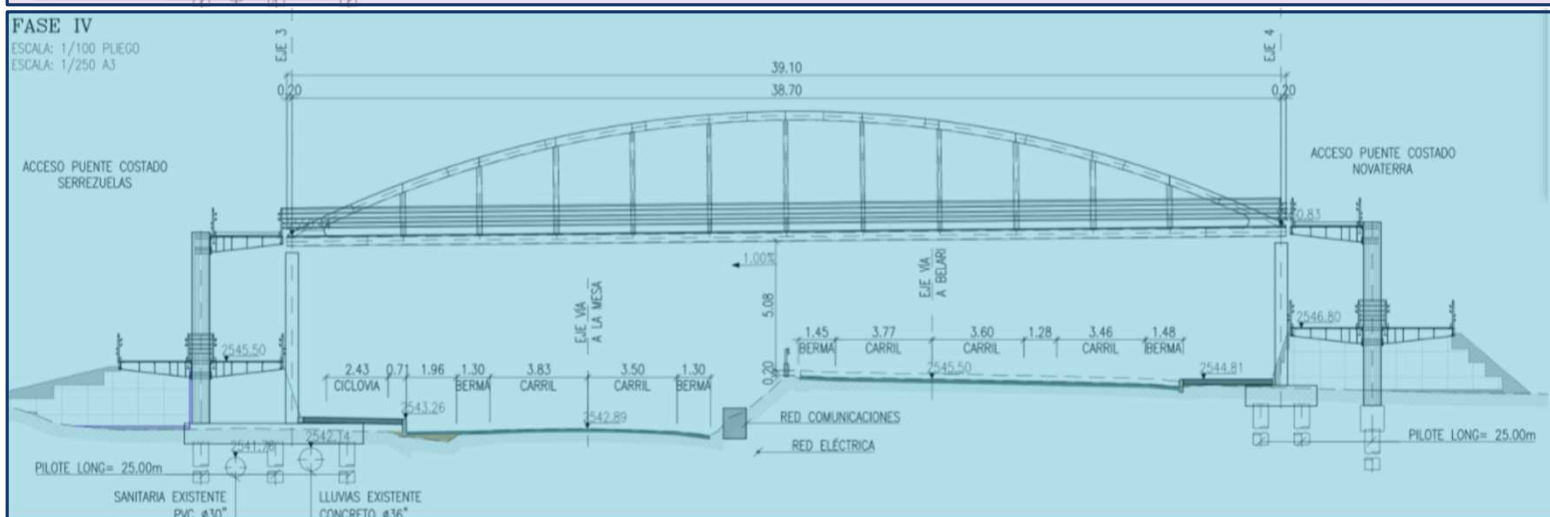

FASE IV:


1. INSTALACIÓN DE BARANDAS EN LAS RAMPAS Y PASARELA.
2. INSTALACIÓN DE PANELES DE MADERPLAST.
3. CONSTRUCCIÓN DE ACERAS
4. CONFORMACIÓN DE TALUDES Y CUBRIRLOS CON MAYA.



ALCALDÍA DE
MOSQUERA



ILUMINACION PUENTE PEATONAL

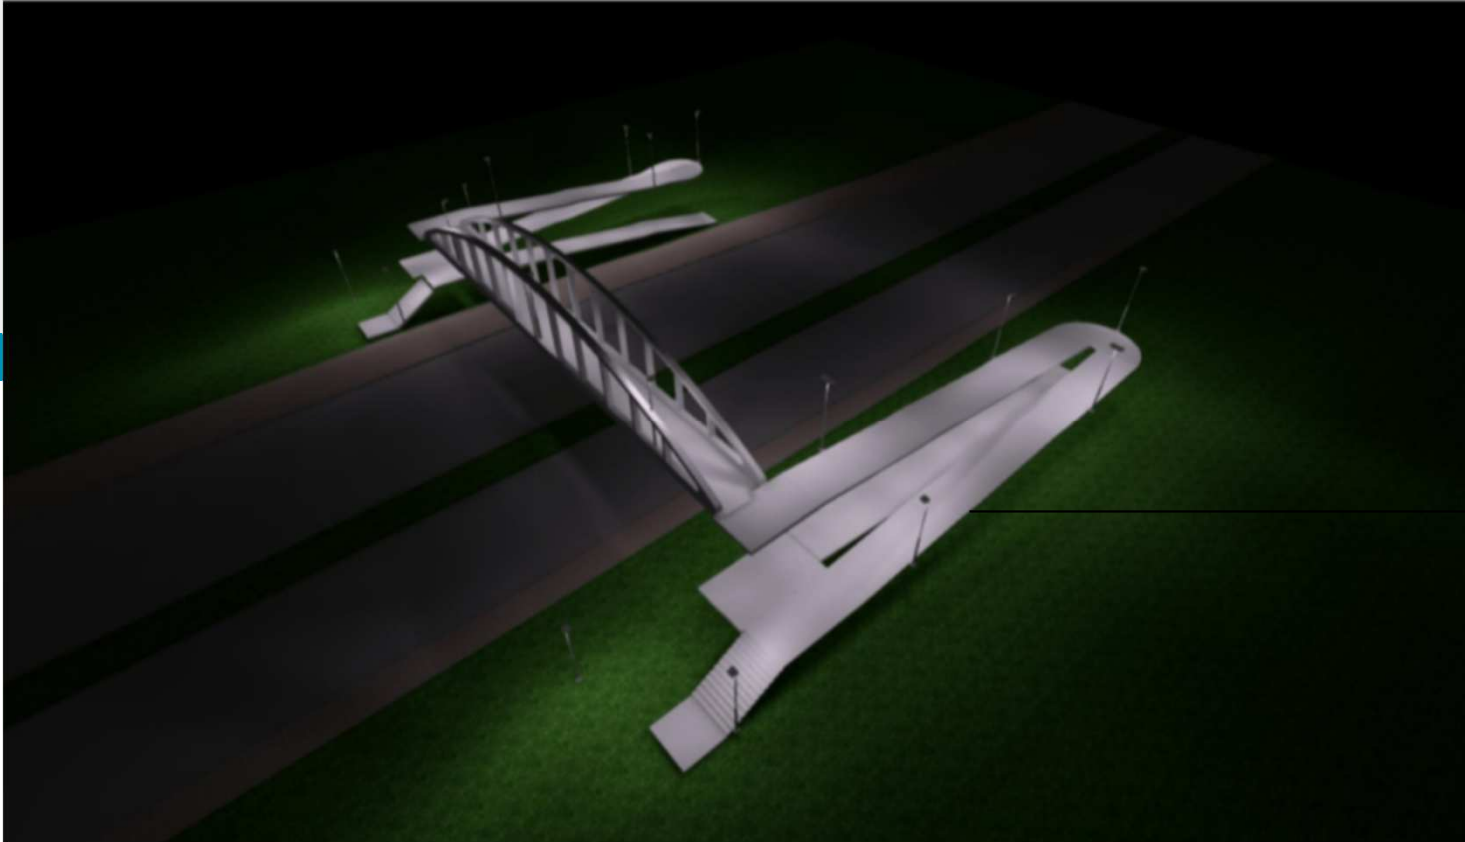


Iluminación solar en apsarela con autonomía de 36 horas de acuerdo a los lineamientos del retilap 2024.



ALCALDÍA DE
MOSQUERA



ILUMINACION PUENTE PEATONAL

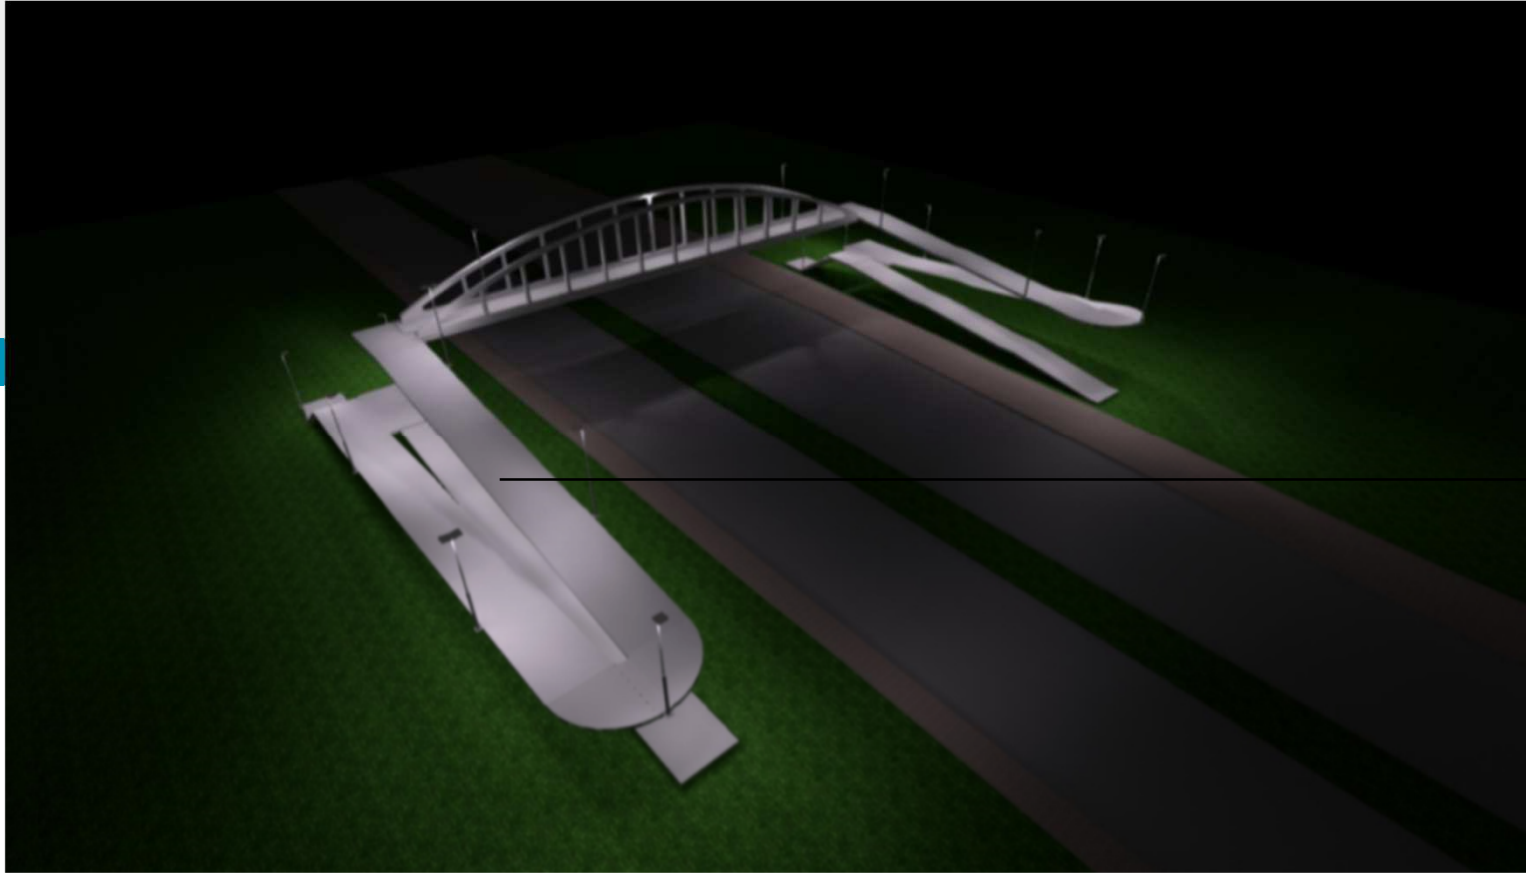


Iluminación eléctrica para las rampas con el fin de garantizar los lúmenes requeridos en todos los espacios.



ALCALDÍA DE
MOSQUERA



ADECUACIONES URBANISMO PUENTE PEATONAL

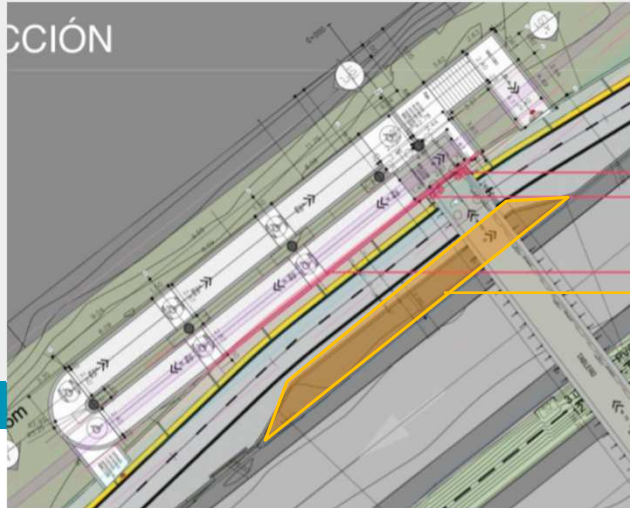

Adecuación del paradero en el costado de Belari, asegurando la continuidad de la ciclorruta y garantizando la seguridad del peatón.





Intervención en el andén con el objetivo de establecer conexión entre el paradero del puente peatonal y los conjuntos del desarrollo urbanístico Novaterra.



ALCALDÍA DE
MOSQUERA



SEÑALIZACION PUENTE PEATONAL

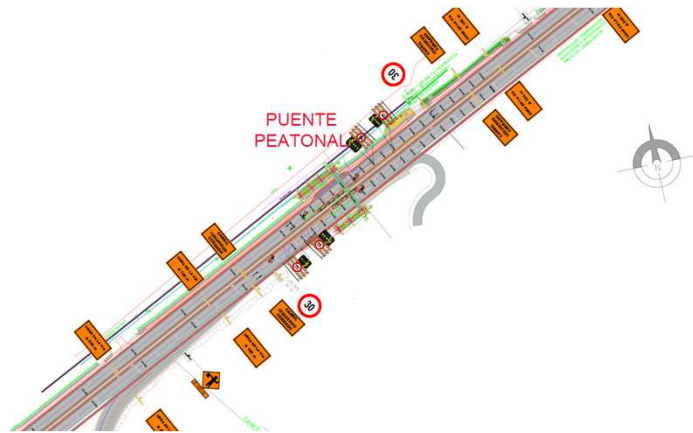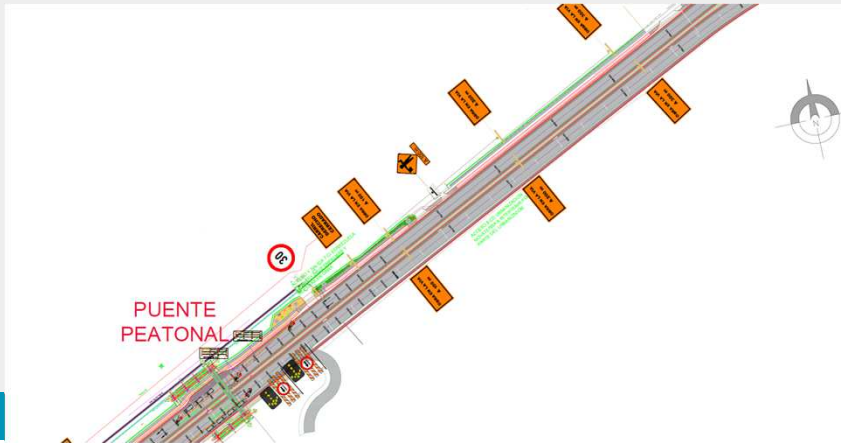

Adecuación de señalización para informar a los usuarios y evitar incidentes, de acuerdo al pmt planteado y aprobado.



ALCALDÍA DE
MOSQUERA



PERMISOS ICCU PUENTE PEATONAL



Funza, Cund.

Señores
INSTITUTO DE CAMINOS Y CONSTRUCCIONES DE CUNDINAMARCA -ICCU
Atn. Dra. Yessenia Herreño Bernal
Directora General
contactenosiccu@cundinamarca.gov.co
Calle 26 No 51-53, Torre Central Piso 6
Bogotá D.C.

Ref.- Rad. ICCU No. Rad. ICCU-E-2025-0005674, Rad. DEVISAB ENT-2025-0000004133 y ENT-2025-0000004137 Solicitud concepto Expediente 531: construcción del puente peatonal BELARÍ Sector La Mesa - Mosquera, PR116+510, Concesión DEVISAB.

Asunto: Respuesta Rad. DEVISAB ENT-2025-0000004133. Y ENT-2025-0000004137 Rad. ICCU-E-2025-0005674

Estimada Doctora Herreño:

En atención al oficio del asunto de la referencia, mediante el cual la Entidad solicitó a DEVISAB S.A.S. emitir el respectivo concepto sobre ocupación temporal del derecho de vía, de acuerdo a la solicitud del permiso de uso, ocupación e intervención realizada por la empresa Constructora Gallas S.A.S., en los términos de la Resolución No. 501 de 2016¹, para el proyecto construcción del puente peatonal BELARÍ Sector La Mesa - Mosquera, PR116+510, de manera atenta nos permitimos dar respuesta en los siguientes términos:

1. Descripción del proyecto:

Construcción del puente peatonal BELARÍ Sector La Mesa - Mosquera, PR116+510.



ALCALDÍA DE
MOSQUERA



BETMAF S.A.S. **SERVINC**
SERVICIOS DE INGENIERÍA

CC CONSORCIO CUNDINAMARCA 044
NIT 901.769.659-2

Señores
INSTITUTO DE CAMINOS Y CONSTRUCCIONES DE CUNDINAMARCA -ICCU
contactenosiccu@cundinamarca.gov.co

Para responder cite este código
CO-CC44-0478-2025-VT
Fecha: 08/07/2025
Anexos: Ninguno.

TEMA: CONTRATO DE CONCESIÓN No. 001 DE 1996 EN EL CORREDOR VIAL CHÍA - MOSQUERA - LA MESA - GIRARDOT, RAMAL A SOACHA Y VÍAS REGIONALES.

ASUNTO: Respuesta oficio ICCU-S-2025-0004080 (Rad. RA-CC44-0593-2025-VT) - Expediente 531: construcción del puente peatonal BELARÍ por la empresa Constructora Gallas S.A.S. - Sector La Mesa - Mosquera, PR 116+510, Concesión DEVISAB.

Cordial saludo,

Atendiendo la solicitud de la entidad, en la que se solicita: *"se pronuncie frente al concepto emitido por la concesión Devisab mediante oficio SALD-2025-01502- Expediente 531, Lo anterior, de acuerdo con la obligación de la cláusula segunda, del contrato ICCU 1241 de 2023"*, el cual, a su vez indica que: *"(...) Por lo anterior, DEVISAB S.A.S. proffiere CONCEPTO FAVORABLE para la expedición de la Resolución de permiso de ocupación temporal del Derecho de vía (...) "* **Negrita y subrayado fuera de texto.**

Por lo que una vez revisada la documentación adjunta se tiene desde la especialidad de tránsito se tiene las siguientes observaciones y/o recomendaciones:

Concepto emitido por DEVISAB:

Frente a la solicitud de que se consagre en la respectiva resolución lo siguiente:

- De acuerdo con el siguiente texto: **"...3. La responsabilidad de la vigilancia y control de la ejecución de los trabajos estará cargo del Instituto de Caminos y Construcciones de Cundinamarca - ICCU y NO se requiere que DEVISAB suscriba actas de aprobación a las obras. No obstante, DEVISAB puede solicitar cualquier adecuación a los trabajos que se adelanten para garantizar la infraestructura vial, en caso de Incumplimiento podrá solicitar a través del ICCU la suspensión de la ejecución de las obras..."**; Esta Interventoría no considera pertinente incluir esta disposición, ya

PRESUPUESTO DEL PUENTE PEATONAL

**INCLUYENDO DISEÑOS TÉCNICOS,
COSTO DE CONSTRUCCIÓN,
MANO DE OBRA, IMPUESTOS**

\$6.600.000.000



ALCALDÍA DE
MOSQUERA



CONSTRUCTORA
CAPITAL
Tu vida, nuestro proyecto.



GRACIAS!!



ALCALDÍA DE
MOSQUERA

